



SUMMARY

I am a BIM Architecture holding 2 years' experience to achieve high career growth through a continuous Process of learning for achieving goal and keeping myself Dynamic in the changing scenario to become a Successful professional and leading to best opportunity to work.

EDUCATION

SRTS (KADAPA)

B. Tech Civil Engineering (JNTU-A)
2018 - 2022

M.V.S.R Jr. COLLEGE (MPC)

Board of Intermediate -Andhra Pradesh
2016 - 2018

Z.P HIGH SCHOOL (SSC)

Board of secondary education-Andhra Pradesh 2015 - 2016

TECHNICAL SKILLS

- REVIT
- NAVISWORKS
- AUTO CAD
- D5 RENDER AND ENSCAPE
- TWINMOTIONS
- CHIEF ARCHITECT
- MICROSOFT OFFICE

PERSONAL DETAILS

- DATE OF BIRTH : 17 Jun 2000
- MARITAL STATUS : Single
- NATIONALITY : Indian

LANGUAGES

- English
- Telugu

PROFESSIONAL EXPERIENCE

AHAMASMI ARCHITECT

BIM Architect | Jul 2024 - Present

PROJECTS:

High Rise Residential, Commercial and Independent, Duplex and
Luxury Villas

ARIJEET RAIKAR DESIGN STUDIO

BIM drafting | Jun2023-Jun2024

PROJECTS:

Luxury Villas and Residence, Commercial and
Independent

ROLES & RESPONSIBILITIES


- I have a good knowledge in Revit Arch, structural and Facade works and I can do Modeling up to LOD 500.
- I can create families in parametric as per the client requirement.
- I can understand the Shop drawings
- I can do sheet work for documentation purpose.
- Model of the building and developed 3D models for construction drawings. I do clash detection and clash reports in Navisworks.
- Collaborated with project team members to create a comprehensive BIM model of the building and developed 3D models for construction drawings.












PORTFOLIO

BIM ARCHITECTURAL
2D & 3D VISUALIZER

SIVA ANGADALA

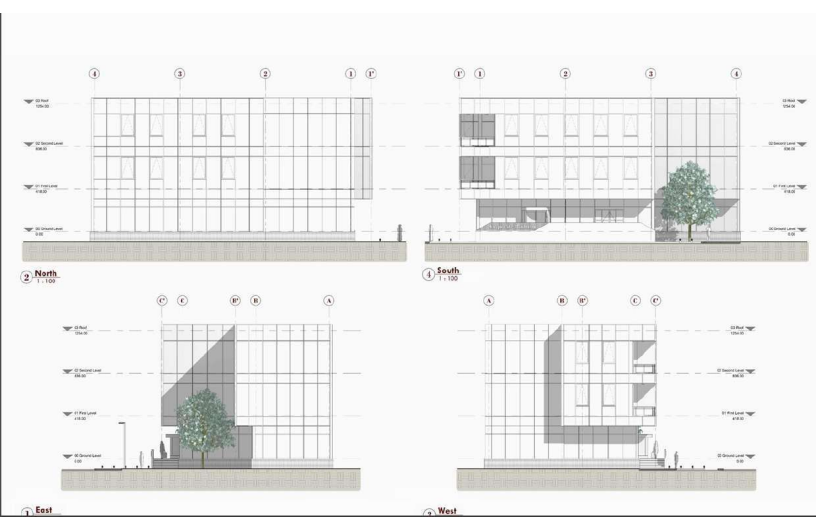

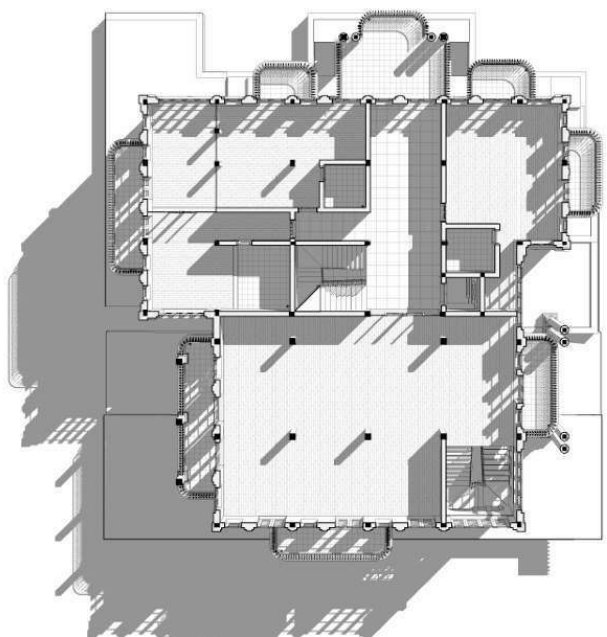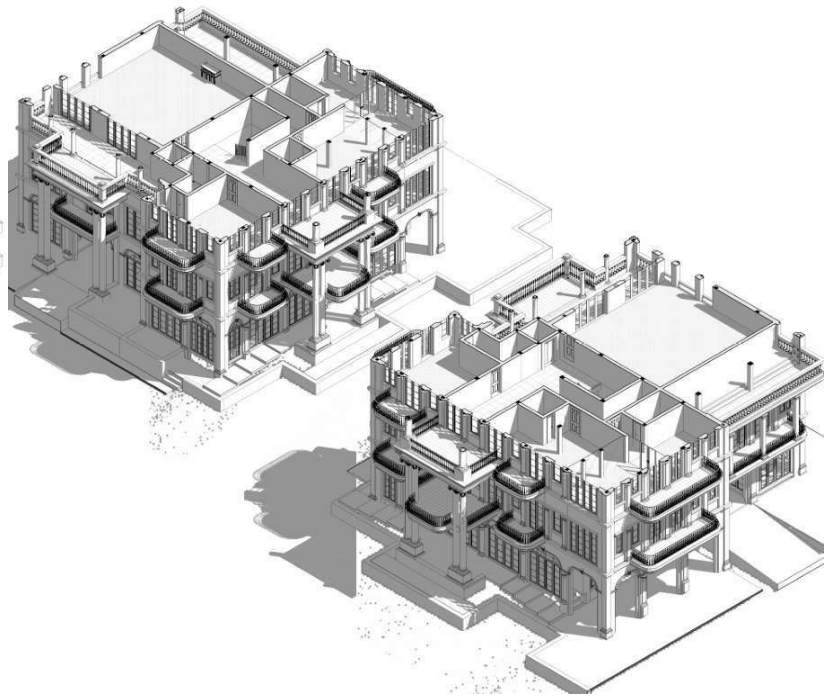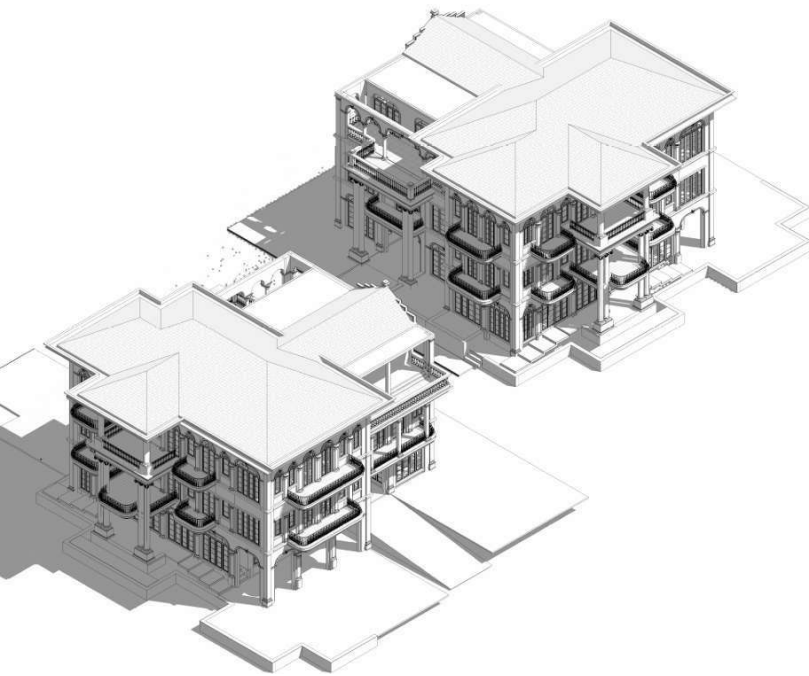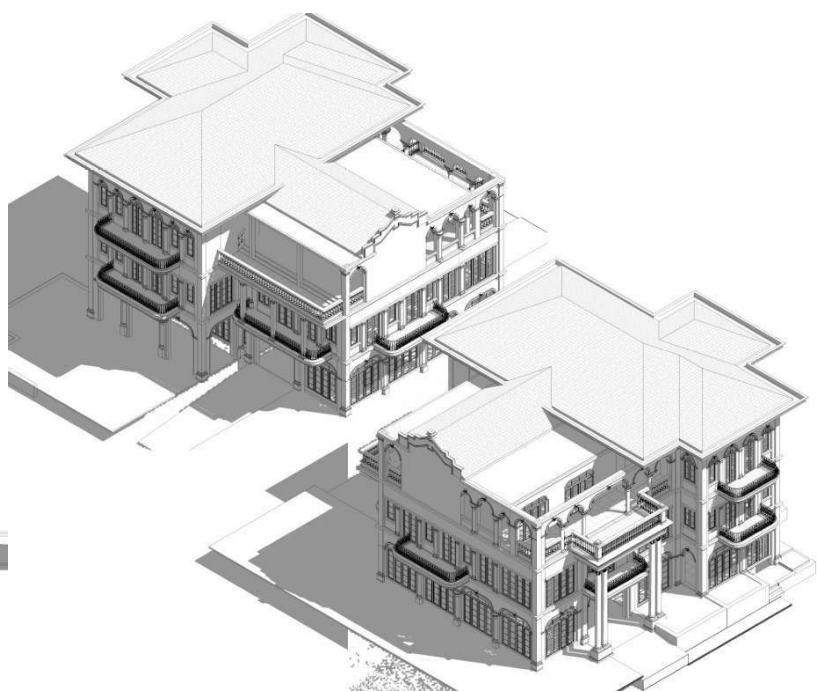

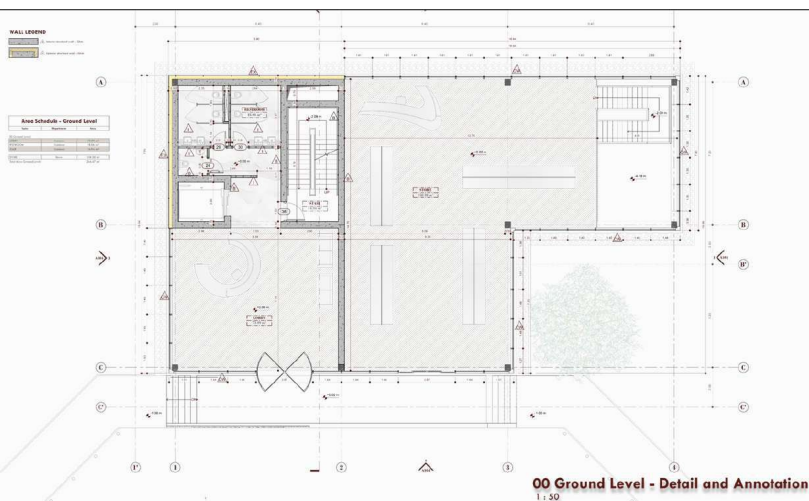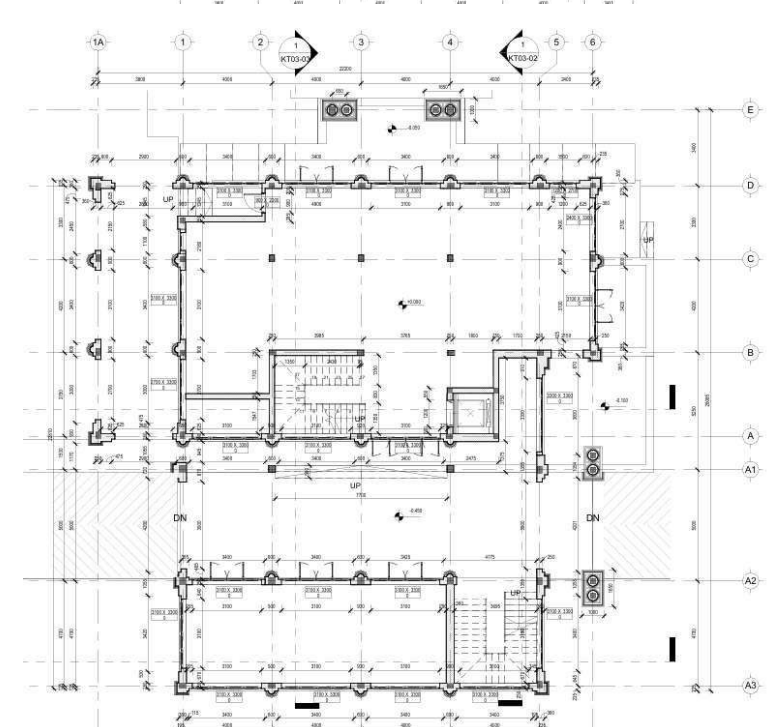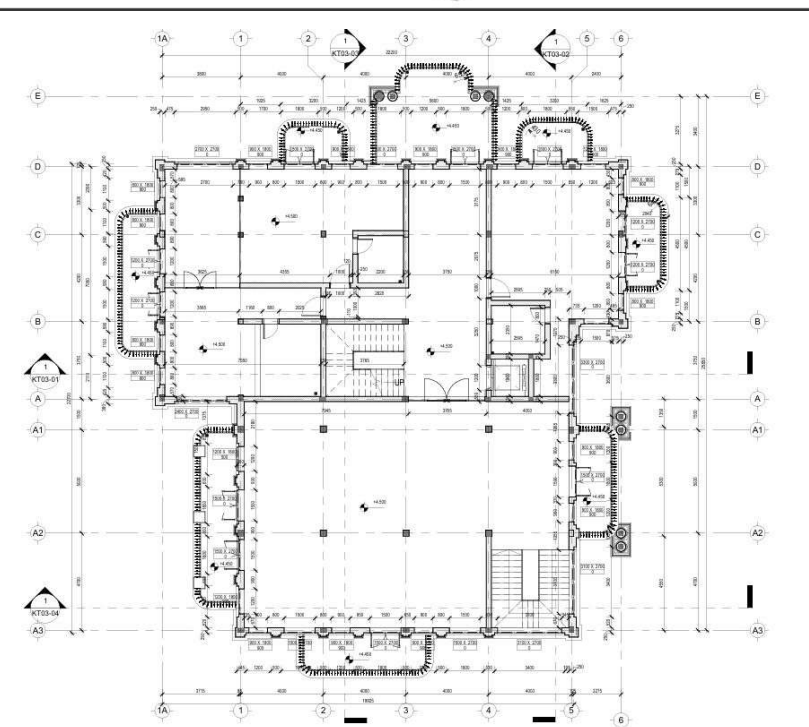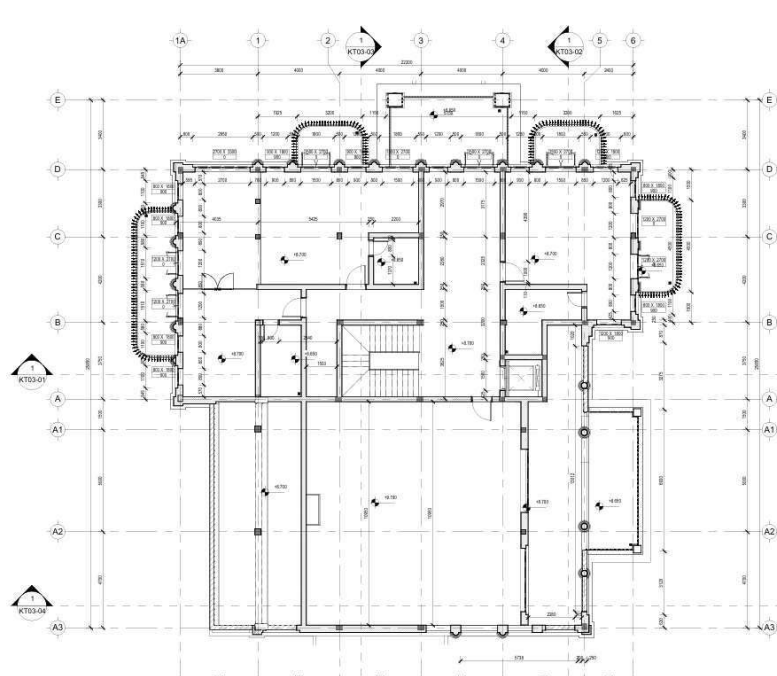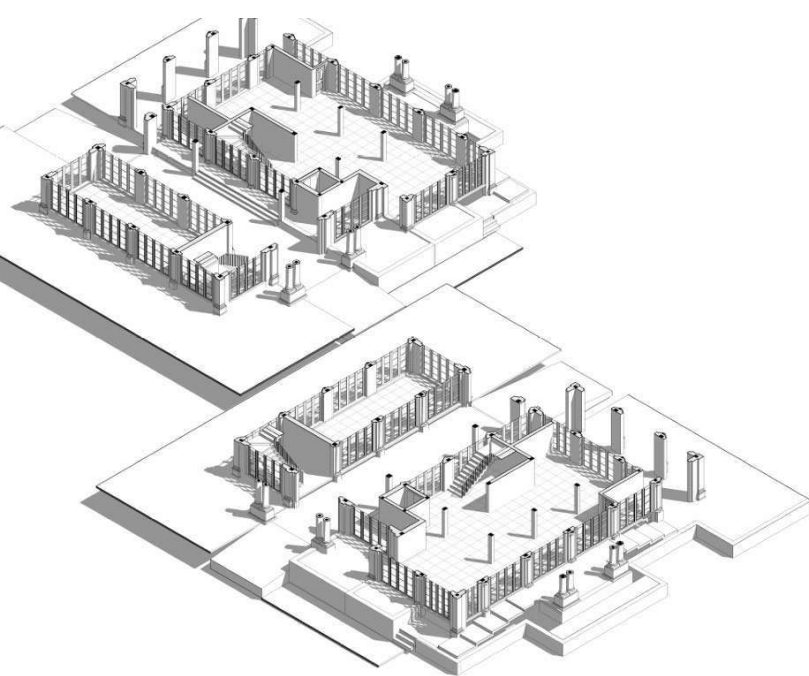

00 Ground Level - Detail and Annotation
1:50





N
FLAT - C
B.A - 1288 SQ.FT.
S.B.A - 1765 SQ.FT.





N
FLAT - B
B.A - 962 SQ.FT.
S.B.A - 1318 SQ.FT.




N
FLAT A
B.A - 1404 SQ.FT.
S.B.A - 1923 SQ.FT.







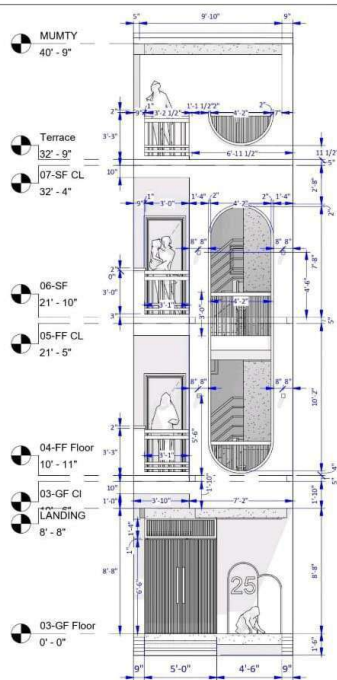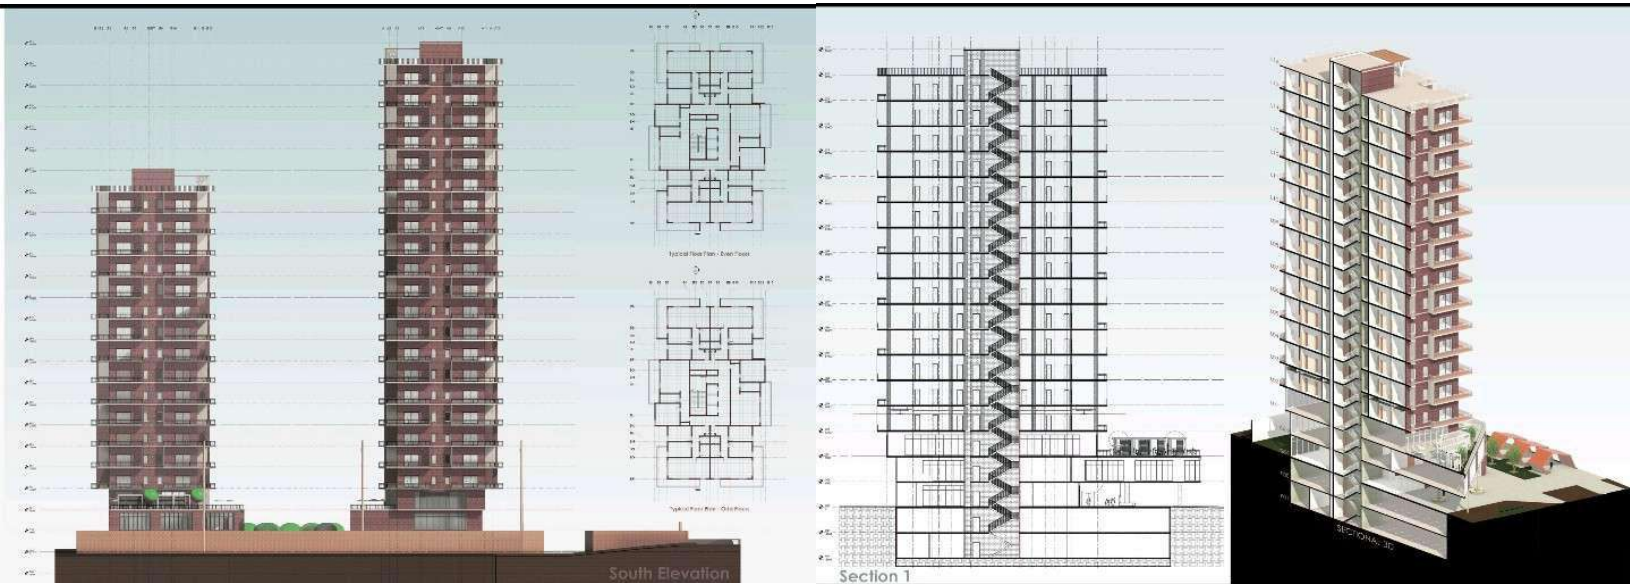


SECOND FLOOR

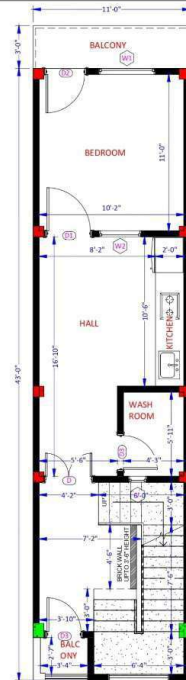

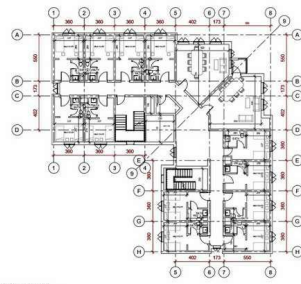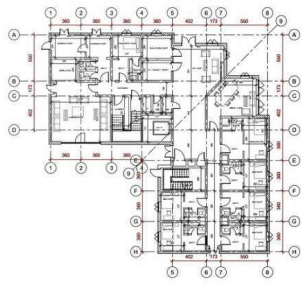




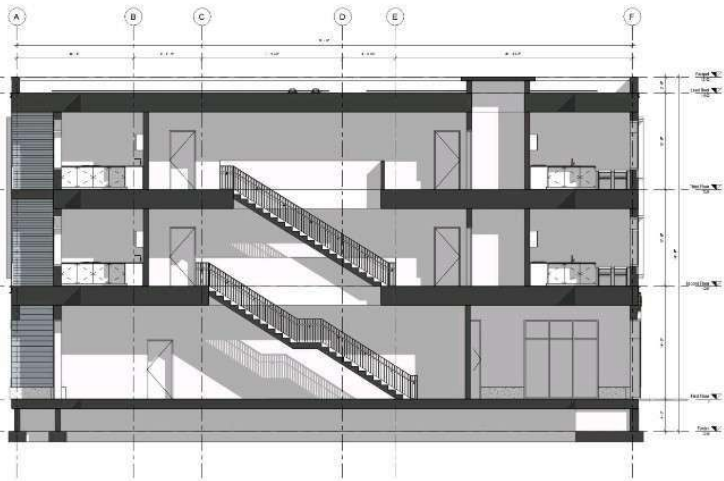


1 Section 1
1:50




1 First Floor Plan
1:50

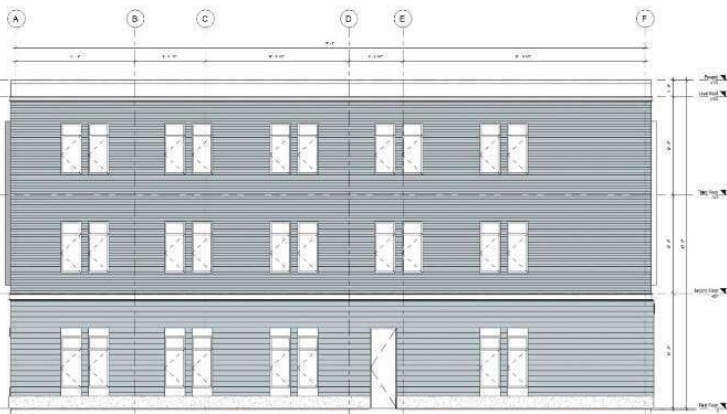

1 South Elevation
1:50

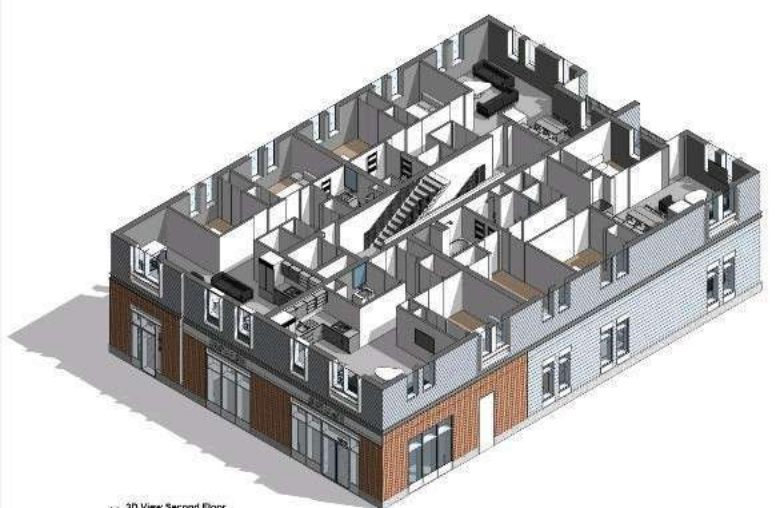

1 3D View Second Floor

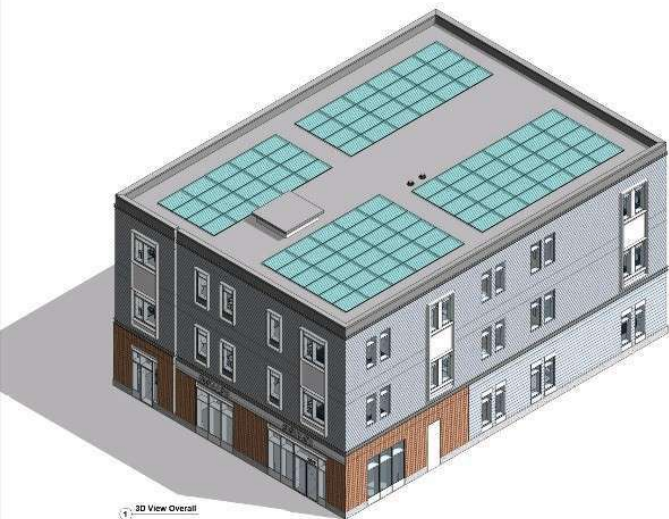

1 3D View Overall

APARTMENT


Owner

3D View Overall

A114




ELEVATIONS

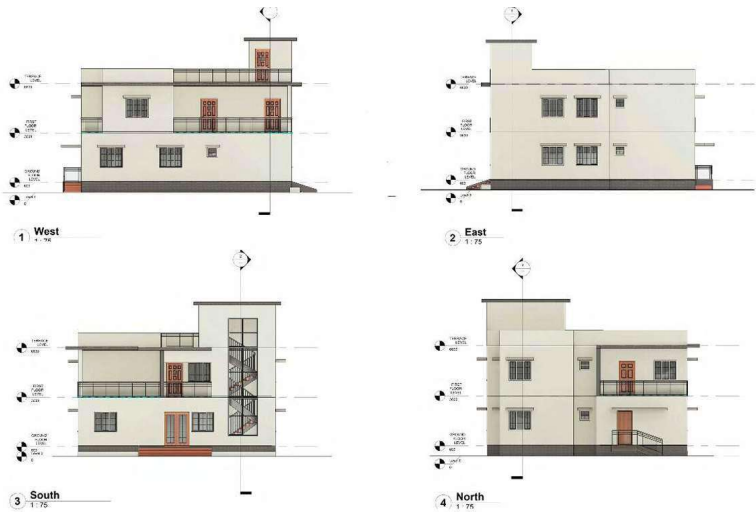


CLASH REPORT



Name	Status	Clashes	New	Active	Reviewed	Approved	Resolved
T01_ARCJ-Set01-[STR]-Set01	Done	121	0	121	0	0	0
T02_ARCJ-Set01-[MEP]-Set01	Done	104	0	104	0	0	0
T03_STRJ-Set01-[MEP]-Set01	Done	27	0	27	0	0	0
T04_MEPJ-Set01-[MEP]-Set01	Done	0	0	0	0	0	0








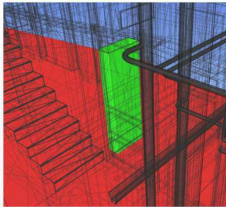


ARCHITECTURAL VS STRUCTURAL CLASH



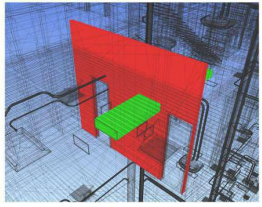


STRUCTURAL VS MEP CLASH

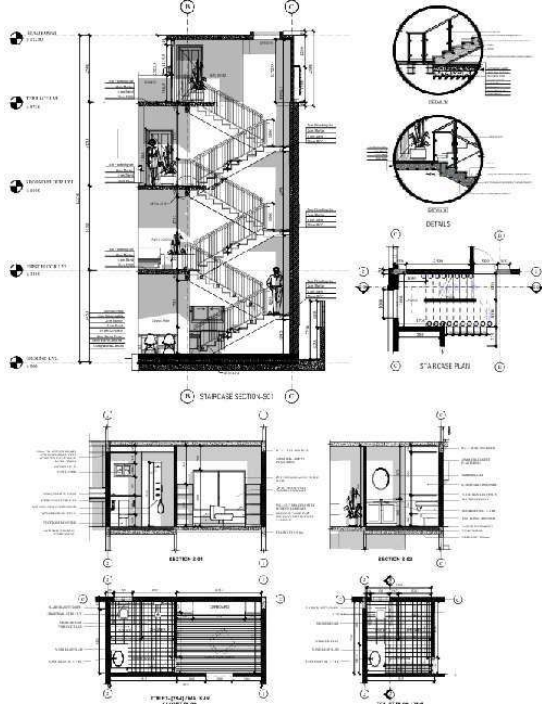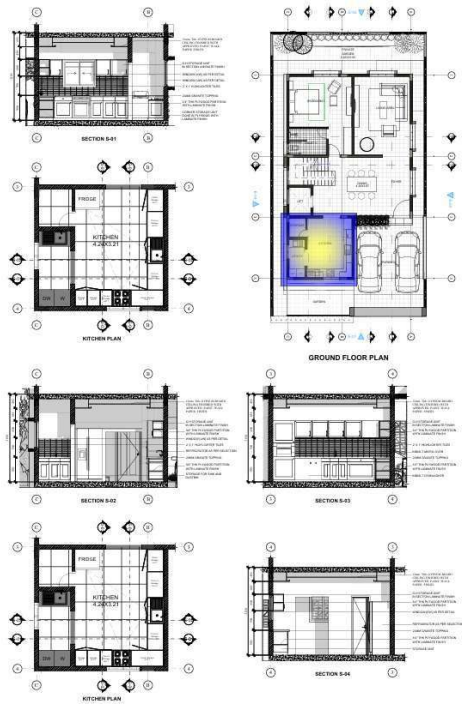

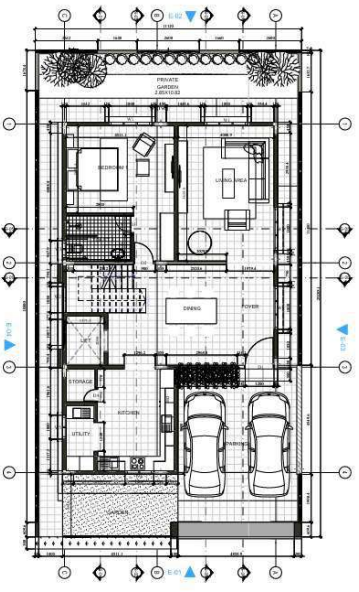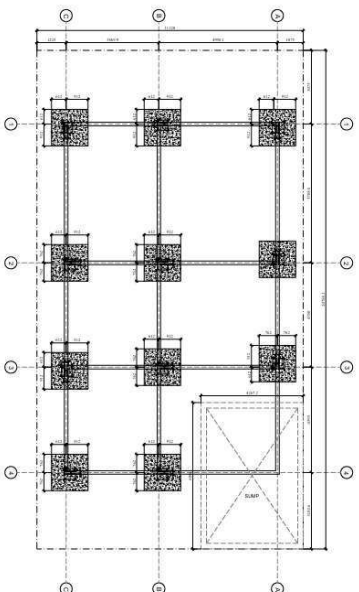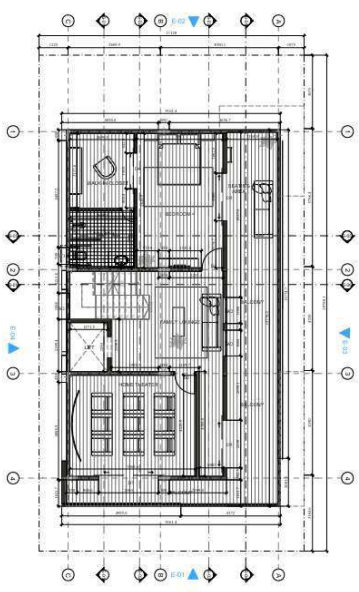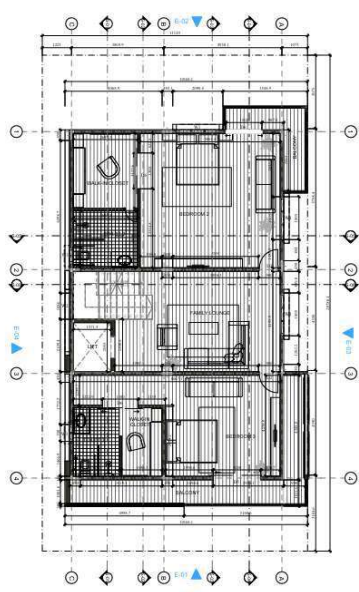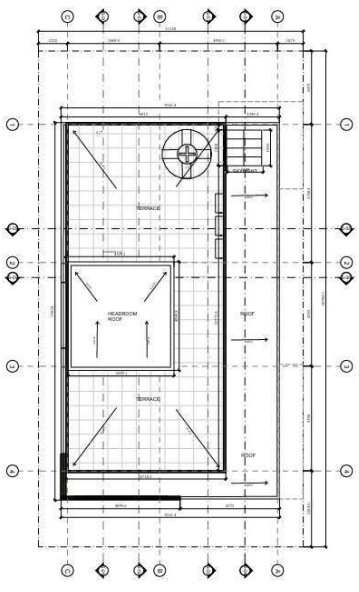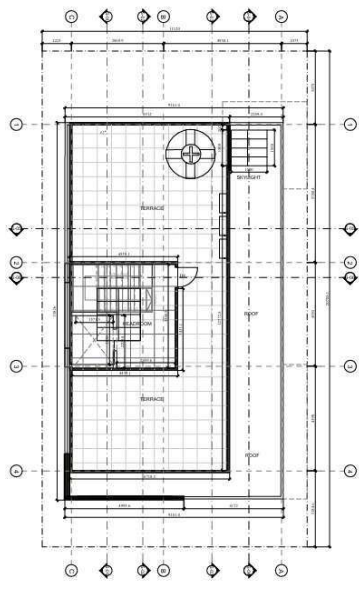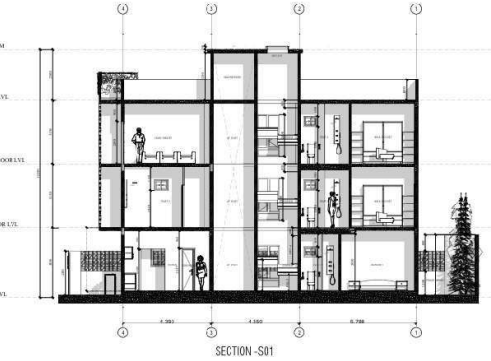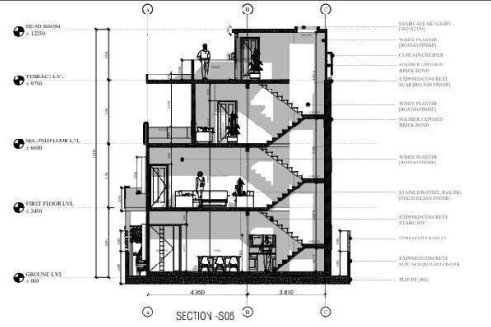

TABLE

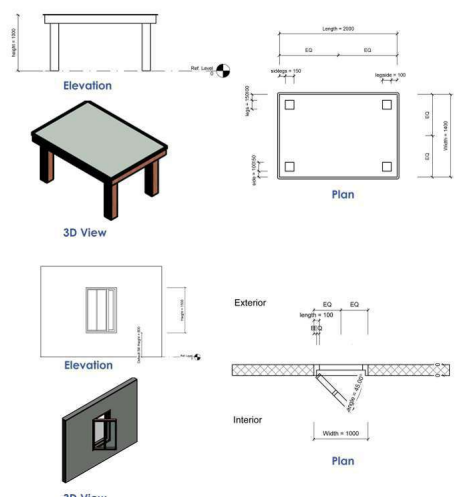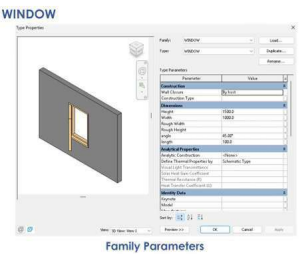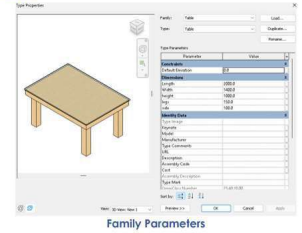

ROOM SCHEDULES

Room Number	Room Name	Level
1	Room	Not Placed
2	Room	2-GF
3	Office 1	1-PL
4	Office 2	1-PL
5	Reception 1	1-PL
6	Reception 2	1-PL
7	Reception 3	1-PL
8	Reception 4	1-PL
9	Reception 5	1-PL
10	Reception 6	1-PL
11	Reception 7	1-PL
12	Reception 8	1-PL
13	Reception 9	1-PL
14	Reception 10	1-PL
15	Reception 11	1-PL
16	Reception 12	1-PL
17	Reception 13	1-PL
18	Reception 14	1-PL
19	Reception 15	1-PL
20	Reception 16	1-PL
21	Reception 17	1-PL
22	Reception 18	1-PL
23	Reception 19	1-PL
24	Reception 20	1-PL
25	Reception 21	1-PL
26	Reception 22	1-PL
27	Reception 23	1-PL
28	Reception 24	1-PL
29	Reception 25	1-PL
30	Reception 26	1-PL
31	Reception 27	1-PL
32	Reception 28	1-PL

DOOR SCHEDULES

Door Number	Door Name	Level
1	Door	Not Placed
2	Door	2-GF
3	Door	1-PL
4	Door	1-PL
5	Door	1-PL
6	Door	1-PL
7	Door	1-PL
8	Door	1-PL
9	Door	1-PL
10	Door	1-PL
11	Door	1-PL
12	Door	1-PL
13	Door	1-PL
14	Door	1-PL
15	Door	1-PL
16	Door	1-PL
17	Door	1-PL
18	Door	1-PL
19	Door	1-PL
20	Door	1-PL
21	Door	1-PL
22	Door	1-PL
23	Door	1-PL
24	Door	1-PL
25	Door	1-PL
26	Door	1-PL
27	Door	1-PL
28	Door	1-PL
29	Door	1-PL
30	Door	1-PL
31	Door	1-PL
32	Door	1-PL




WINDOW SCHEDULES

Window Number	Window Name	Level
1	Window	Not Placed
2	Window	2-GF
3	Window	1-PL
4	Window	1-PL
5	Window	1-PL
6	Window	1-PL
7	Window	1-PL
8	Window	1-PL
9	Window	1-PL
10	Window	1-PL
11	Window	1-PL
12	Window	1-PL
13	Window	1-PL
14	Window	1-PL
15	Window	1-PL
16	Window	1-PL
17	Window	1-PL
18	Window	1-PL
19	Window	1-PL
20	Window	1-PL
21	Window	1-PL
22	Window	1-PL
23	Window	1-PL
24	Window	1-PL
25	Window	1-PL
26	Window	1-PL
27	Window	1-PL
28	Window	1-PL
29	Window	1-PL
30	Window	1-PL
31	Window	1-PL
32	Window	1-PL

DOOR & WINDOW LEGEND

Mark	Door & Window Type	Size in cm (W x H)	Type Image	Remarks
MD	Curtain Wall Door	180 X 230		Main Entrance
D-01	External Glass Door	180 X 210		Reception Entrance
D-02	Wooden Door	90 X 210		Office Doors
D-03	Wooden Door	80 X 210		Toilet Doors
W-01	Glass Window	175 X 200		All Office Spaces


CALLOUTS

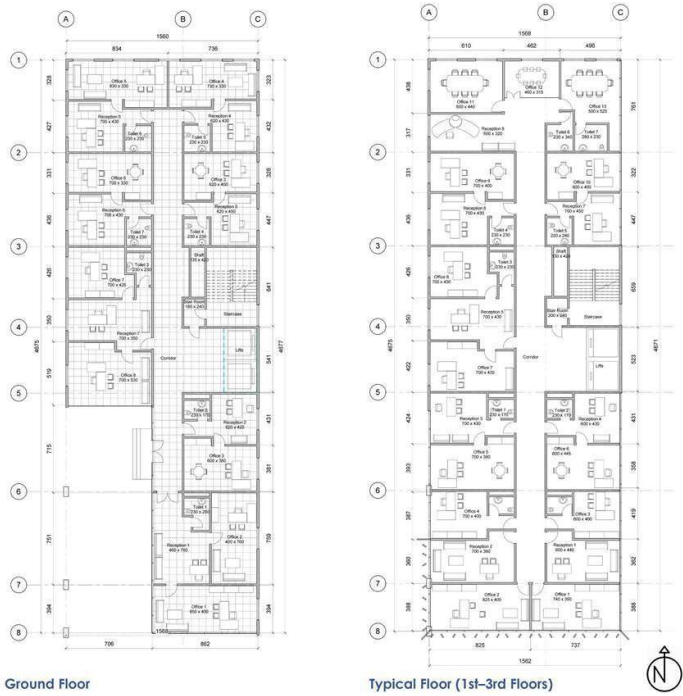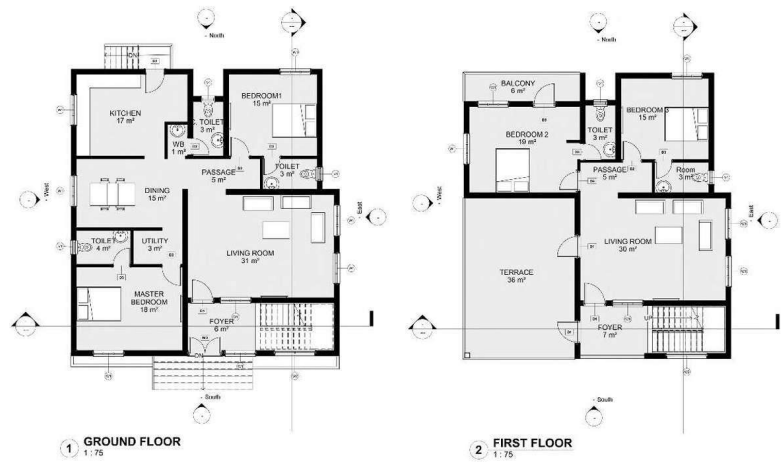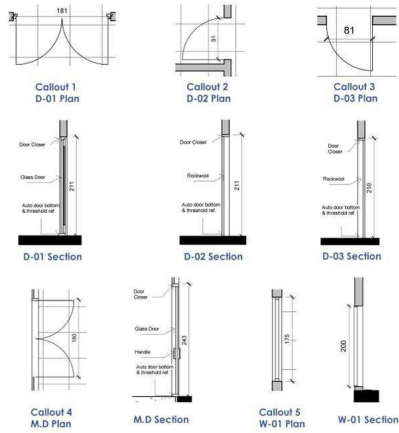


REFLECTED CEILING PLAN (RCP)



STAIRCASE DETAIL

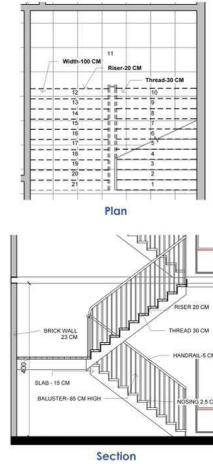

ROOM ZONING

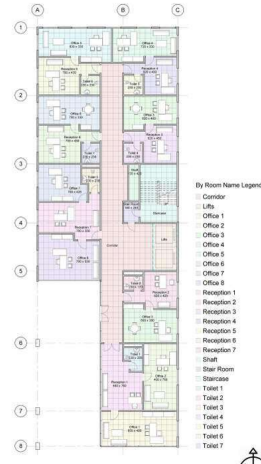

EXPLODED VIEW

